


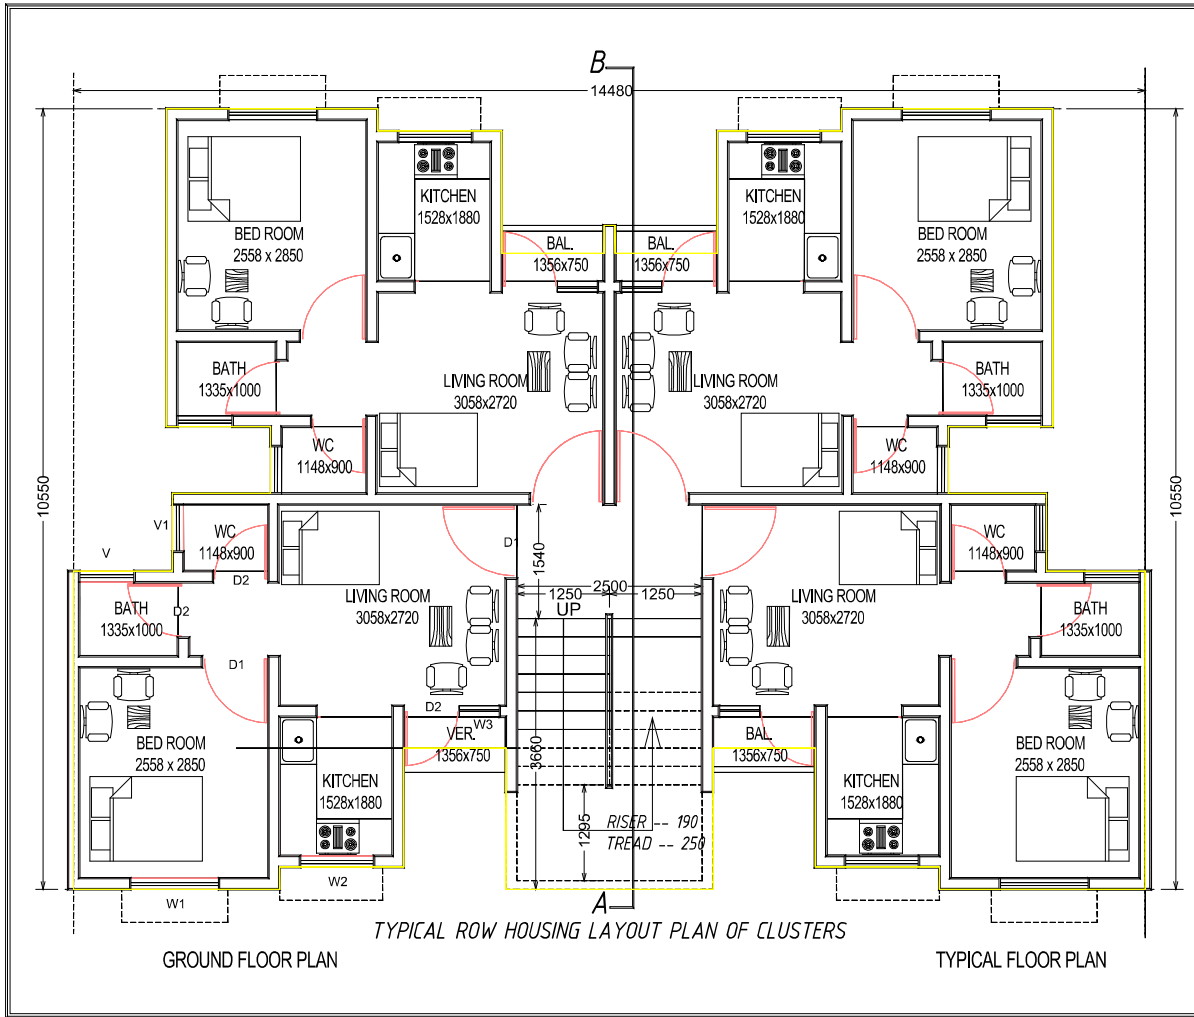

UPAVP

ARCHITECTURAL AND PLANNING SECTION
NEELGIRI COMPLEX, INDIRA NAGAR
LUCKNOW-226016
Email : updv@sancham.in

ISO-9001:2000

STD.DRG.FOR CLUSTER

SHEET NO. -

DRG.NO. TYPICAL UNIT PLAN

NOTE

1. ALL DIMENSIONS ARE IN MM.
2. FIGURED DIMENSION SHOULD BE FOLLOWED.
3. ALL R.C.C WALLS ARE 150MM TH.

SCHEDULE OF DOORS & WINDOWS

SL.NO	TYPE	WIDTH	HEIGHT	REMARKS
1.	D1	900	2000	-
2.	D2	750	2000	-
3.	W1	1000	1200	CILL AT - 800
4.	W2	900	1000	CILL AT - 1000
5.	W3	578	1200	CILL AT - 800
6.	V	750	450	CILL AT - 1550
7.	V1	600	450	CILL AT - 1550

AREA DETAILS (in Sqm)-

PLINTH AREA (FOUR UNITS)- 121.50

PLINTH AREA(one unit with cirr. area) -30.375

TITLE

**STANDARD BUILDING PLAN
(FOR G+3)**

CONSULTANTS

**ARCHITECTURE & PLANNING SECTION,
U.P.AVAS EVAM VIKAS PARISHAD,LUCKNOW.**

SCALE - 1 :

DATE : 19.03.2010

DESIGNED BY

P.K.MAURYA

D.ARCH. A.I.T.

ARCH. ASSIST.

HEMA AGARWAL

D. ARCH. A.I.T.

ASSTT.ARCH.PLANNER

AJIT DUBEY

B. ARCH.

ARCHITECT PLANNER

SANJEEV KASHYAP

B. PLANNING (MADRAS) ARCH. PLANNING I.I.T.

SENIOR ARCHITECT PLANNER

C.P.SHARMA

M. EXP. A.I.T.

CHIEF ARCHITECT PLANNER

DEEPAK KUMAR

JAE

AVAS AYUKT